RISING MAIN FROM PS-1 TO HILL TANK - LONG SECTION

PIPE: DN600 DUCTILE IRON K9, PN25 DESIGN FLOW 320 L/s (2 DUTY + 1 STANDBY PUMPS)

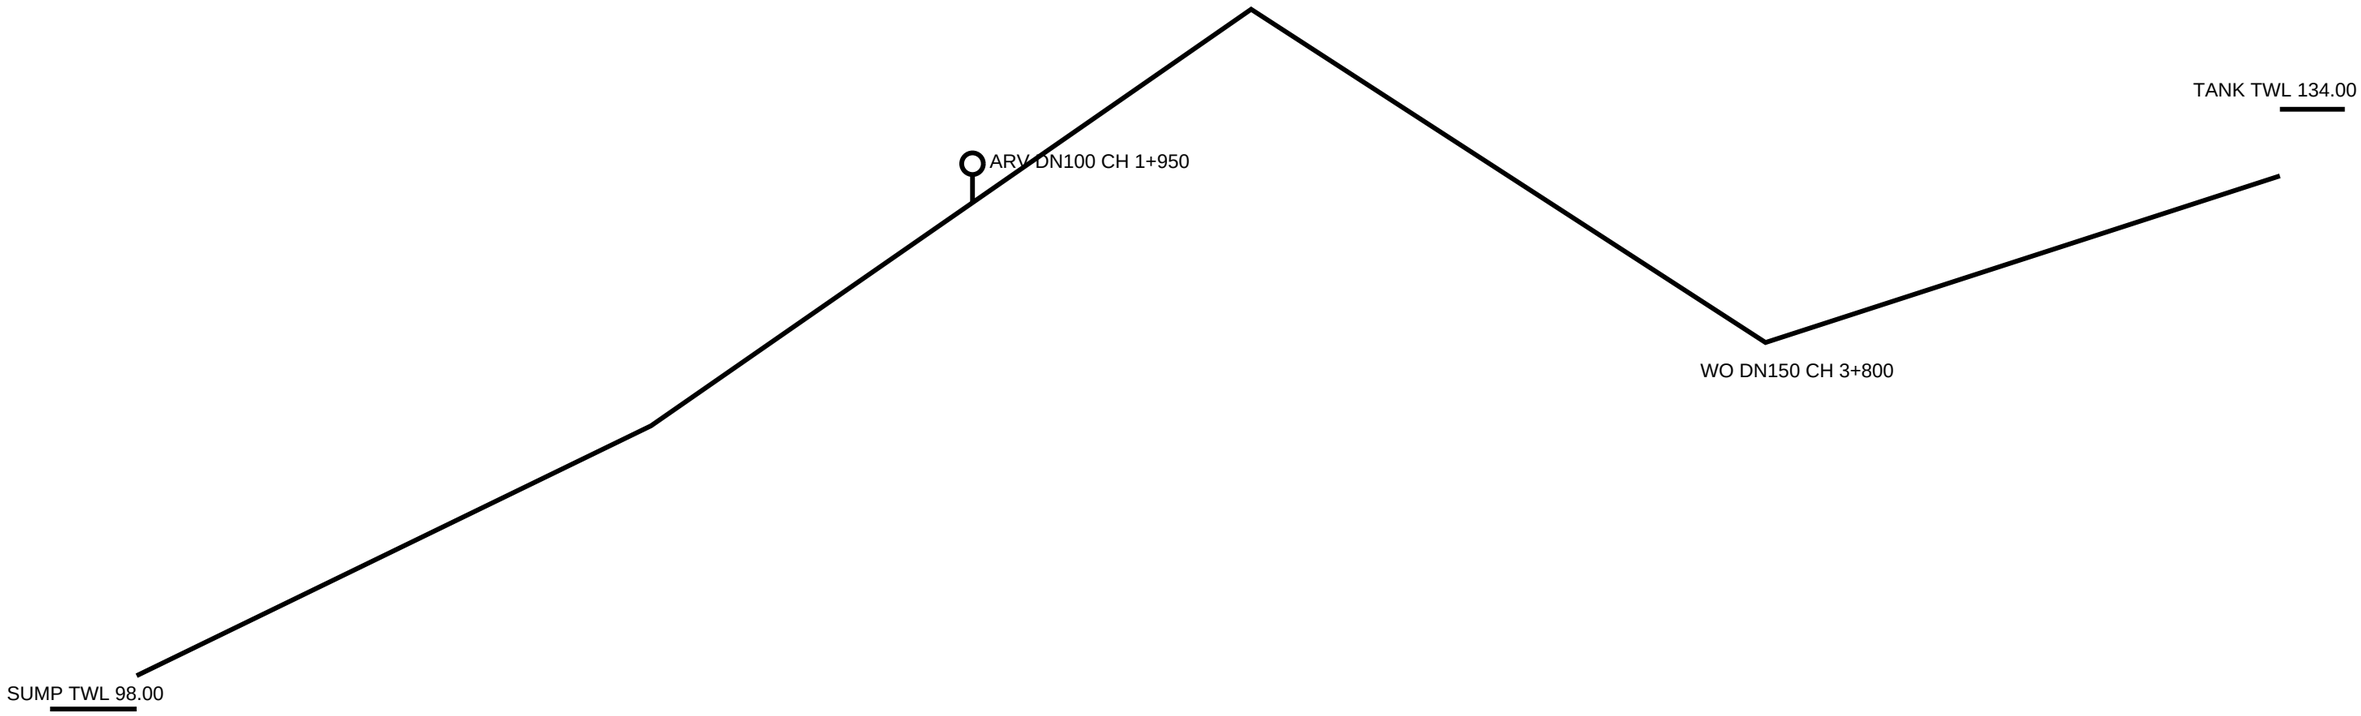

CHAINAGE (m)	0	1200	2600	3800	5000
PIPE INVERT (m)	100.00	115.00	140.00	120.00	130.00
GROUND LEVEL (m)	101.50	116.50	141.50	121.50	131.50

PUMPS: 2 DUTY, 160 L/s @ 47 m EACH, 1480 rpm